


TP. HÀ NỘI - HUYỆN ƯNG HOÀ

XÃ VIÊN NỘI
TỜ SỐ 1 (301572-2-b)

XÃ VIÊN NỘI - TỜ SỐ 1

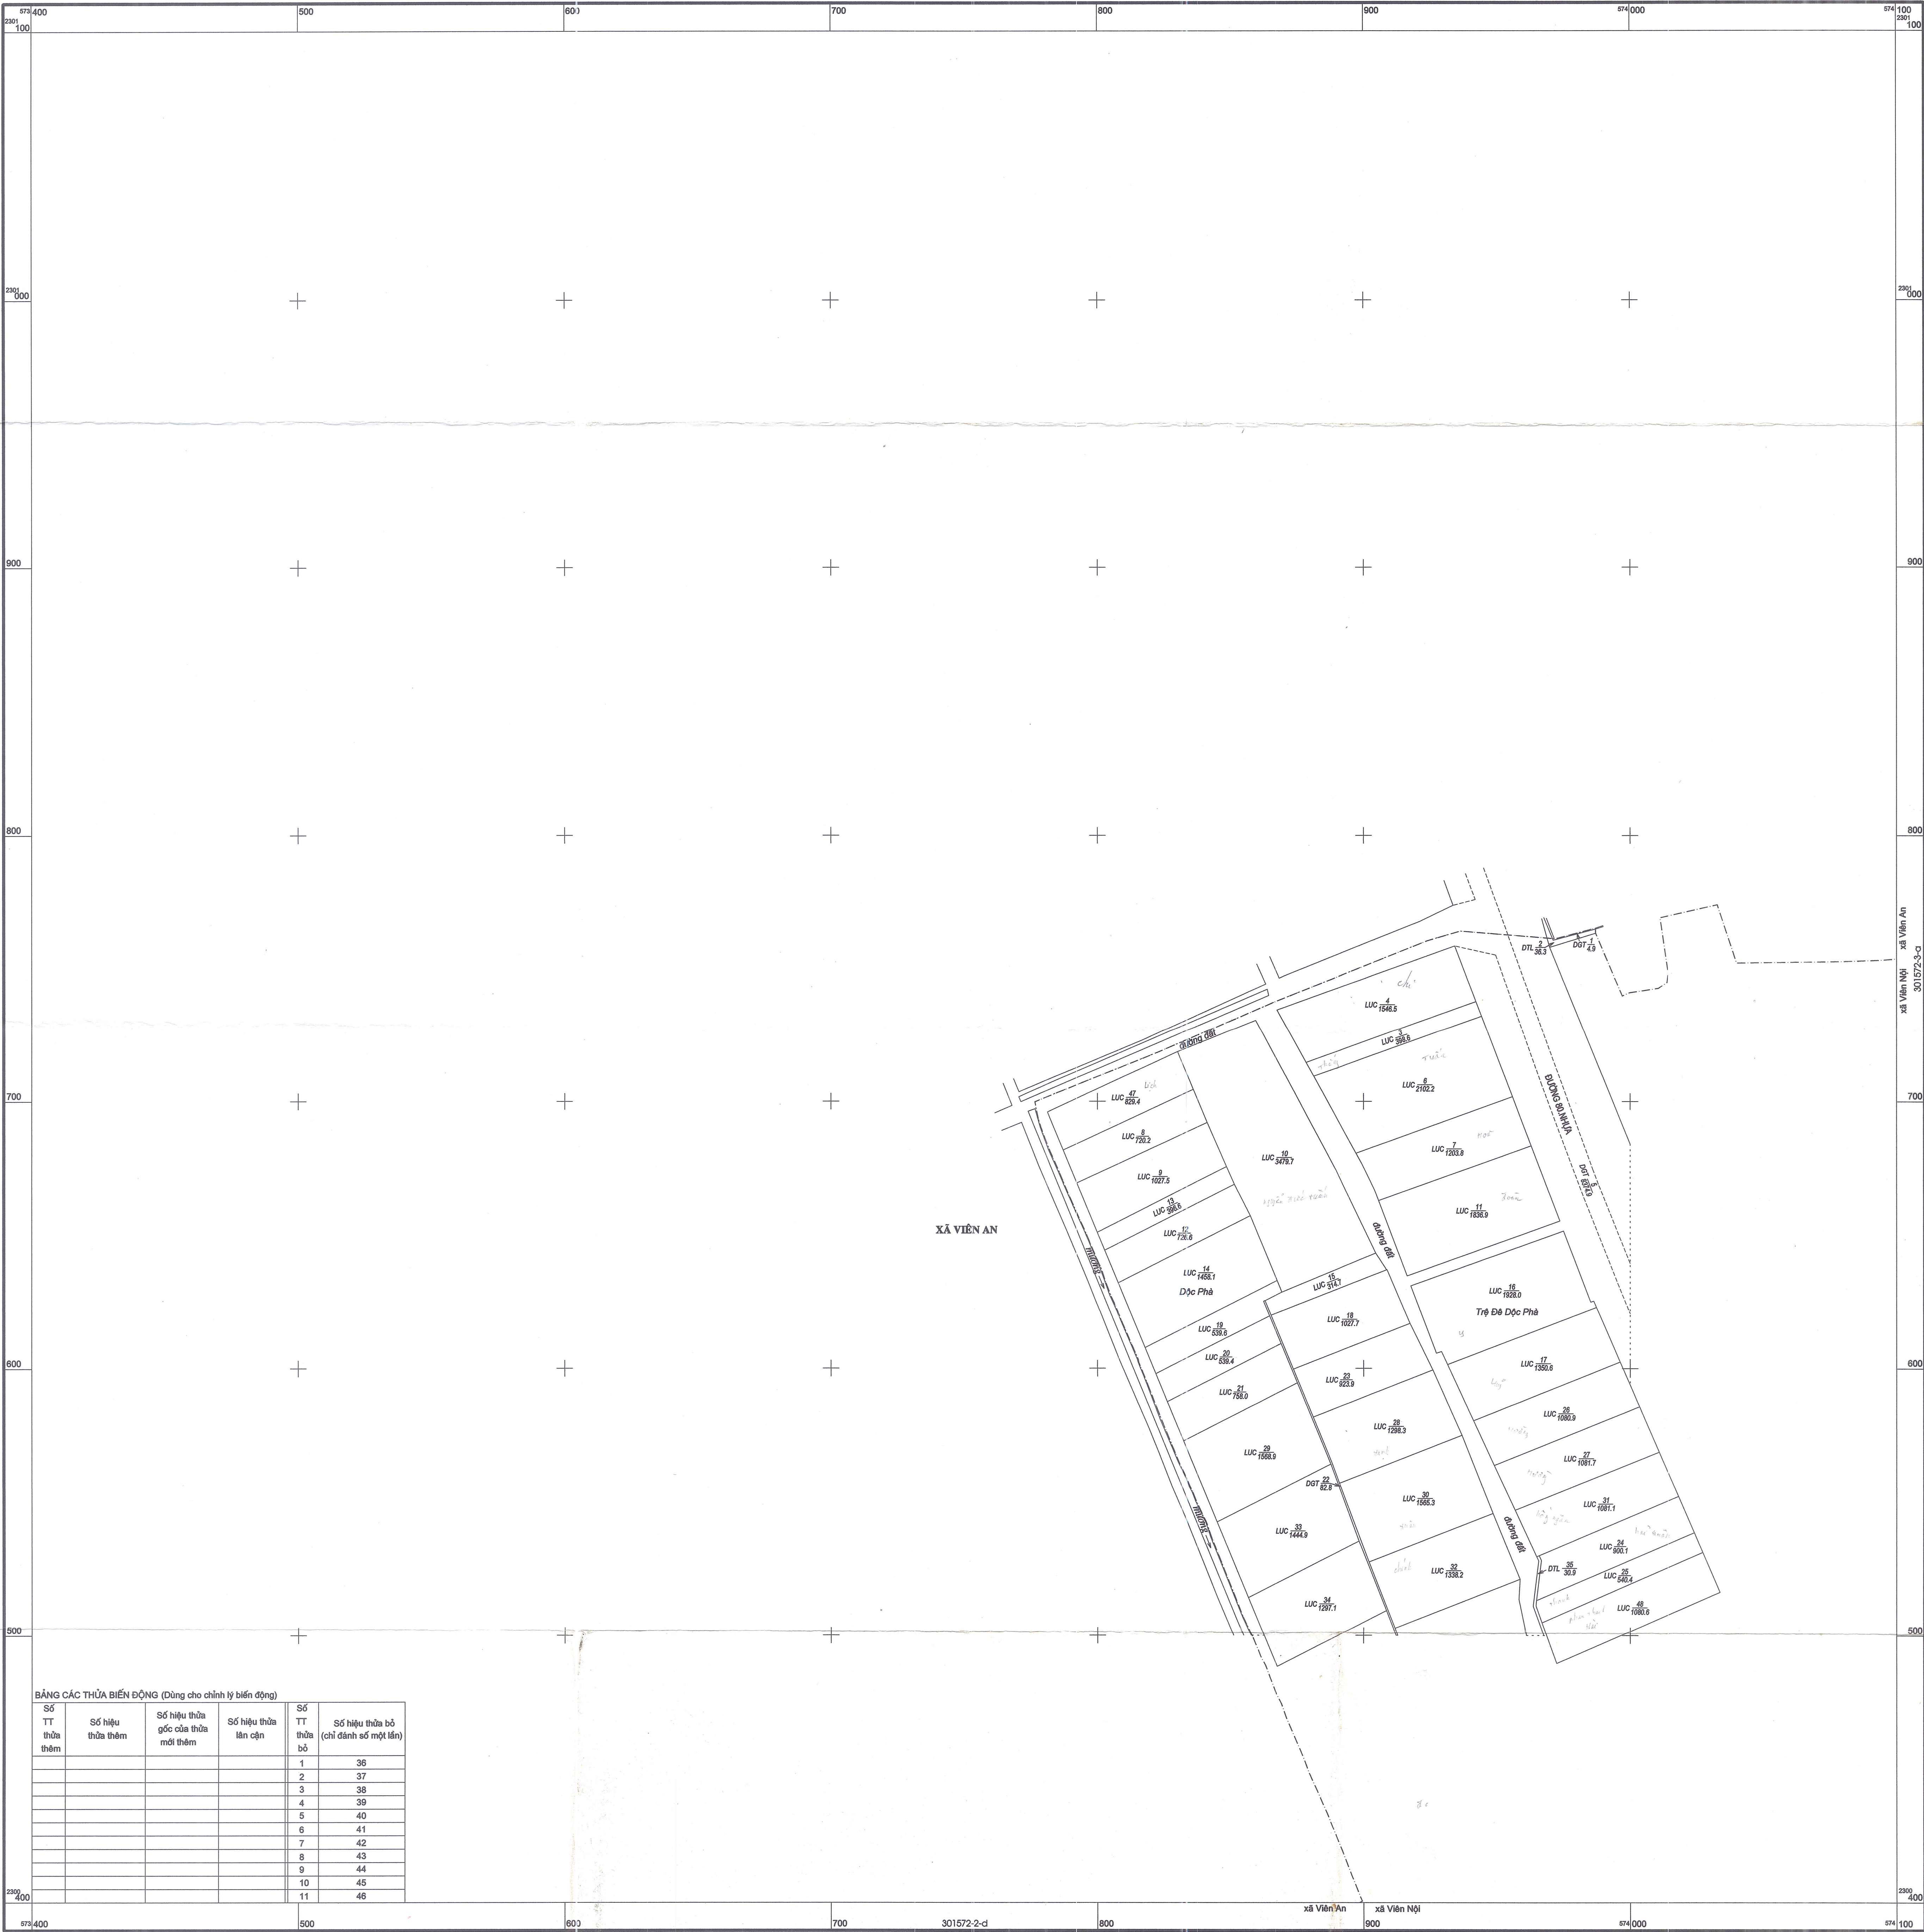

BẢNG CÁC THUẢ BIẾN ĐỘNG (Dùng cho chỉnh lý biến động)

Số TT thửa thêm	Số hiệu thửa thêm	Số hiệu thửa gốc của thửa mới thêm	Số hiệu thửa lân cận	Số TT thửa bỏ	Số hiệu thửa bỏ (chỉ đánh số một lần)
				1	36
				2	37
				3	38
				4	39
				5	40
				6	41
				7	42
				8	43
				9	44
				10	45
				11	46

Đo vẽ tháng 6 năm 2014.
Cơ quan đo vẽ: Công ty cổ phần Hưng Quốc

Kiểm tra tháng 1 năm 2014
Cơ quan kiểm tra: Trung tâm Kỹ thuật - Công nghệ địa chính




GIÁM ĐỐC
Trần Ngọc Tuấn



PHÓ GIÁM ĐỐC
Đào Ngọc Huyền

TỈ LỆ 1:1000

1 cm trên bản đồ bằng 10 m trên thực địa

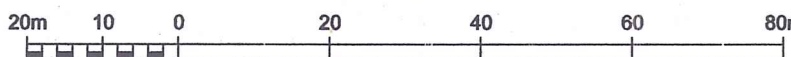

Công nhận đo vẽ đúng hiện trạng
Ngày 28 tháng 1 năm 2014
Chủ tịch UBND xã Viên Nội
(Ký tên, đóng dấu)



CHỦ TỊCH
Trương Văn Hải

Duyệt, ngày 31 tháng 1 năm 2014
Sở Tài nguyên và Môi trường TP. Hà Nội
(Ký tên, đóng dấu)



PHÓ GIÁM ĐỐC
Nguyễn Minh Mười

THÀNH 30 TỜ
TỜ SỐ 1
Tổng số thửa: 37

Đạt chất lượng