



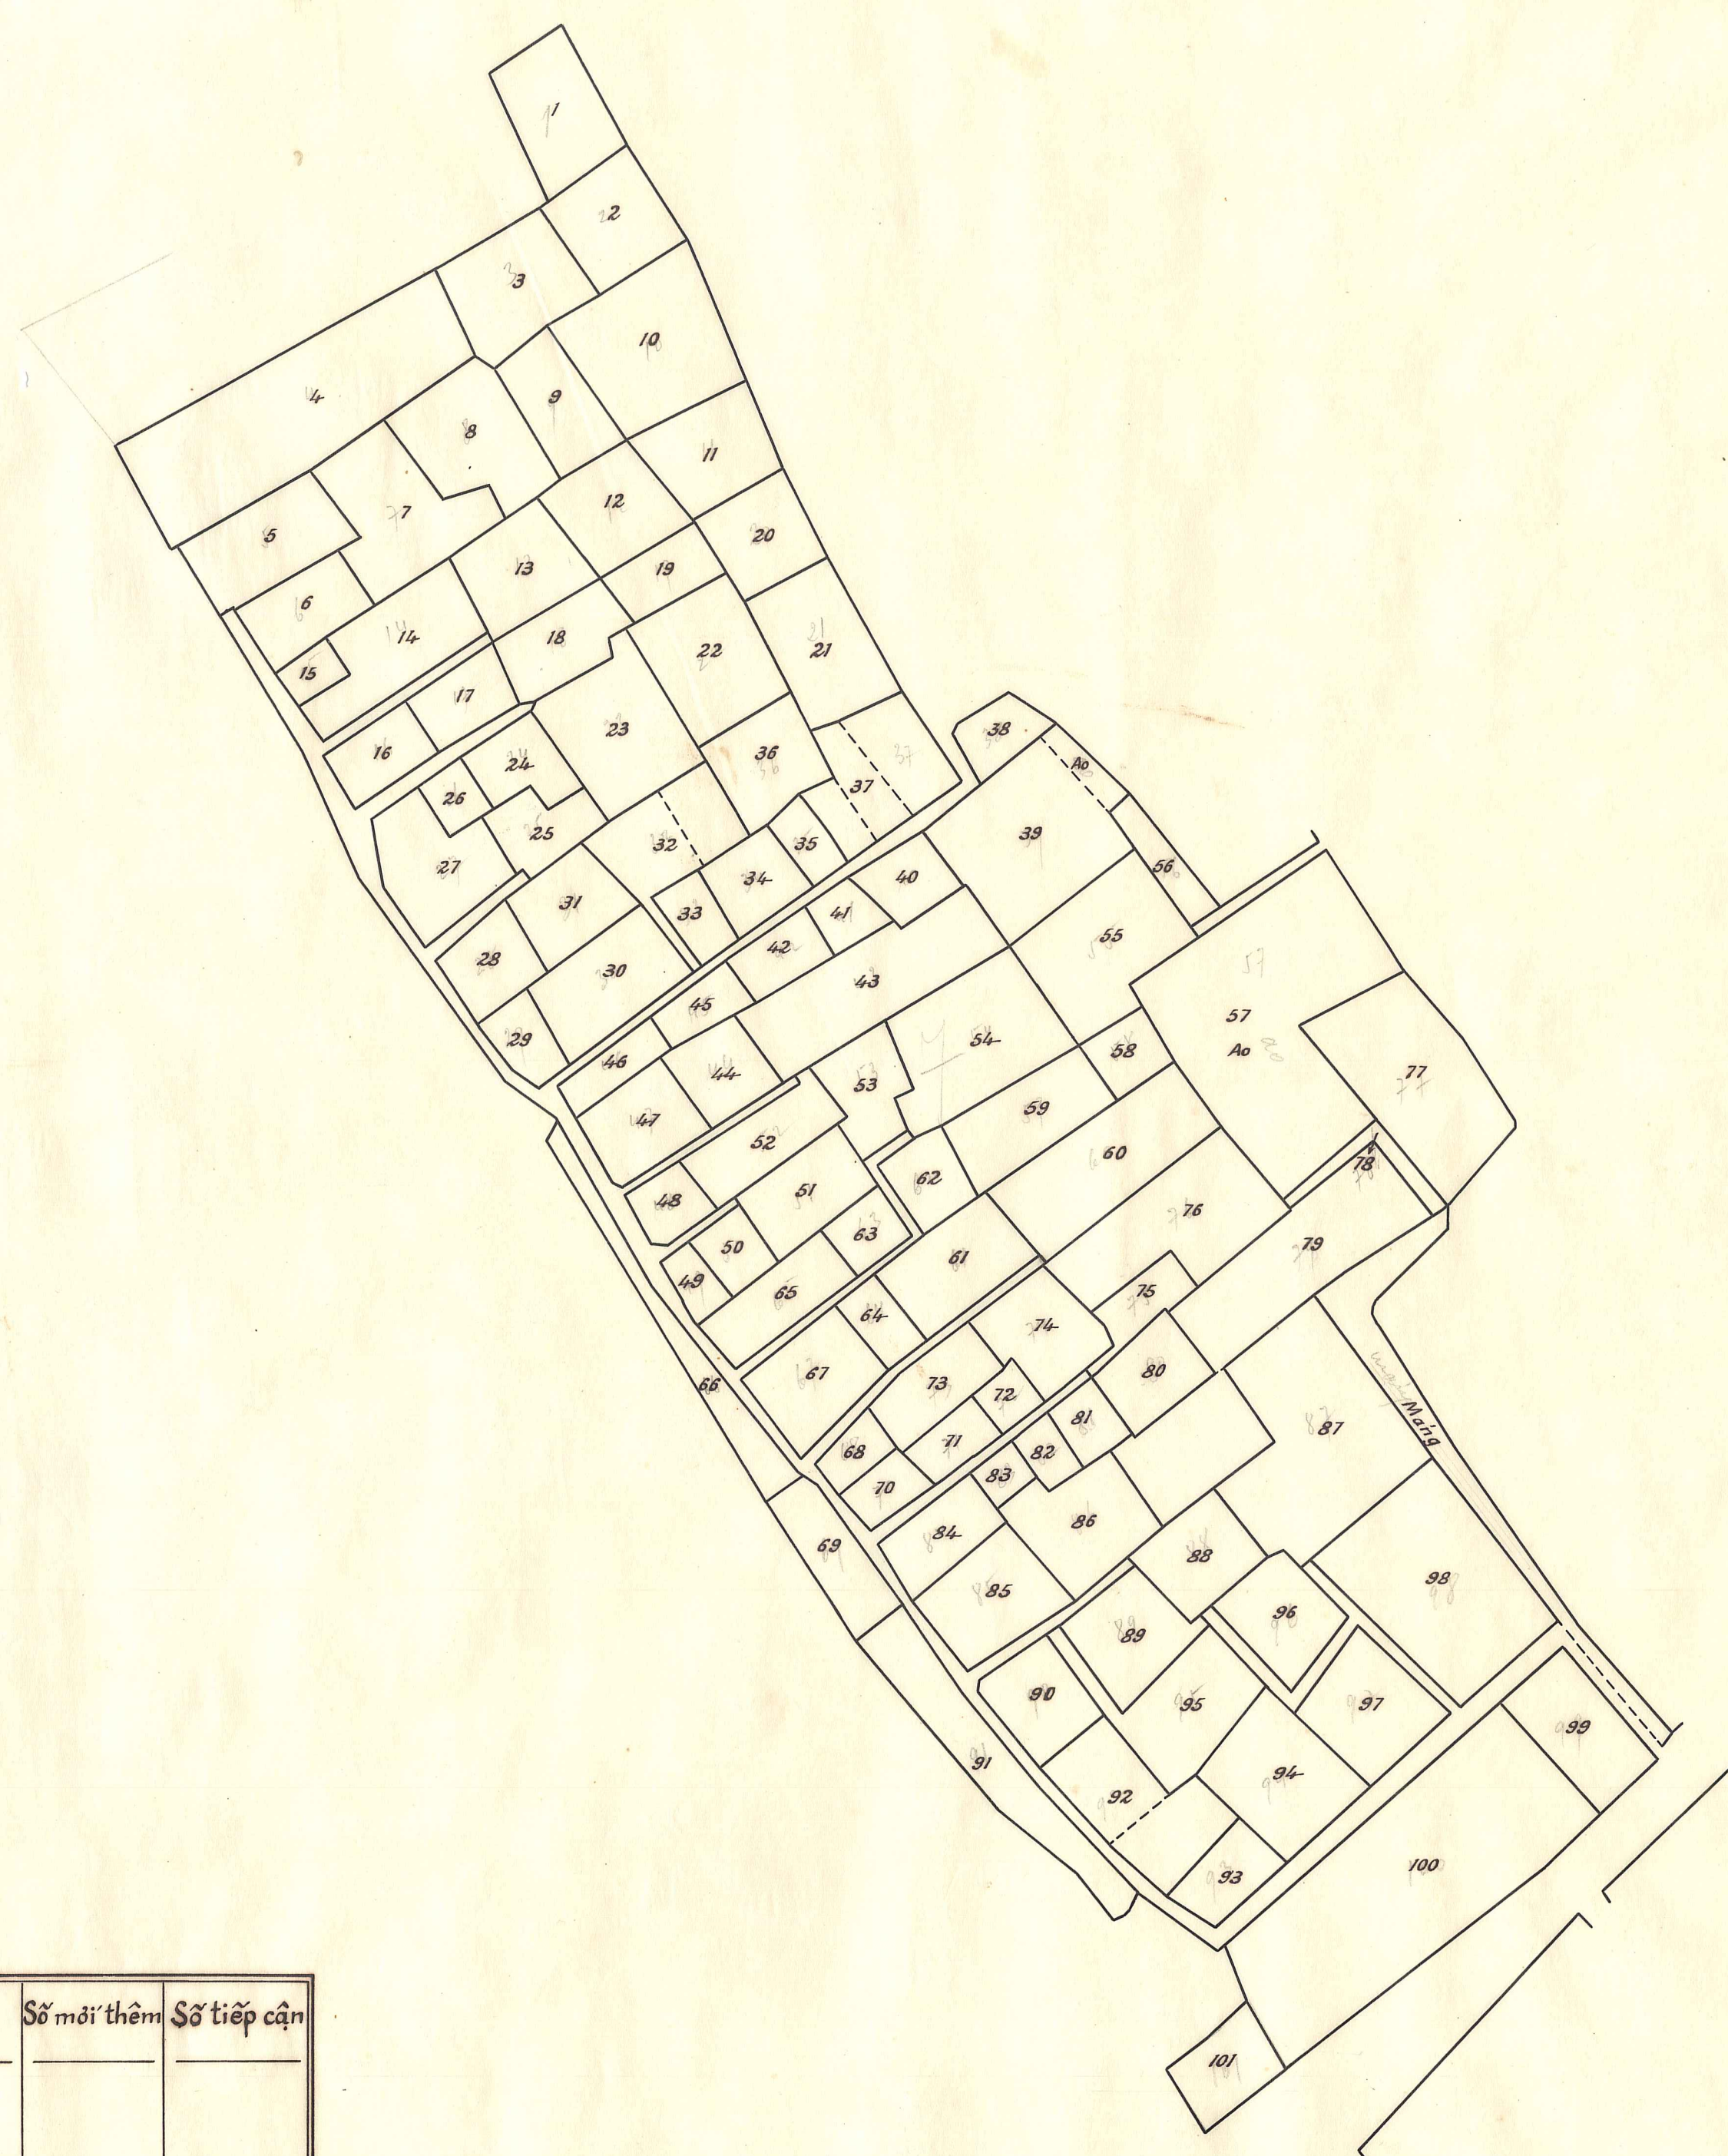

Số bỏ đi	Số mới thêm	Số tiếp cận

Đoặc ngày 15 tháng 6 năm 1967
Đặc viên: Trần Lương Duyên

Đặc viên: Trần Lương Duyên

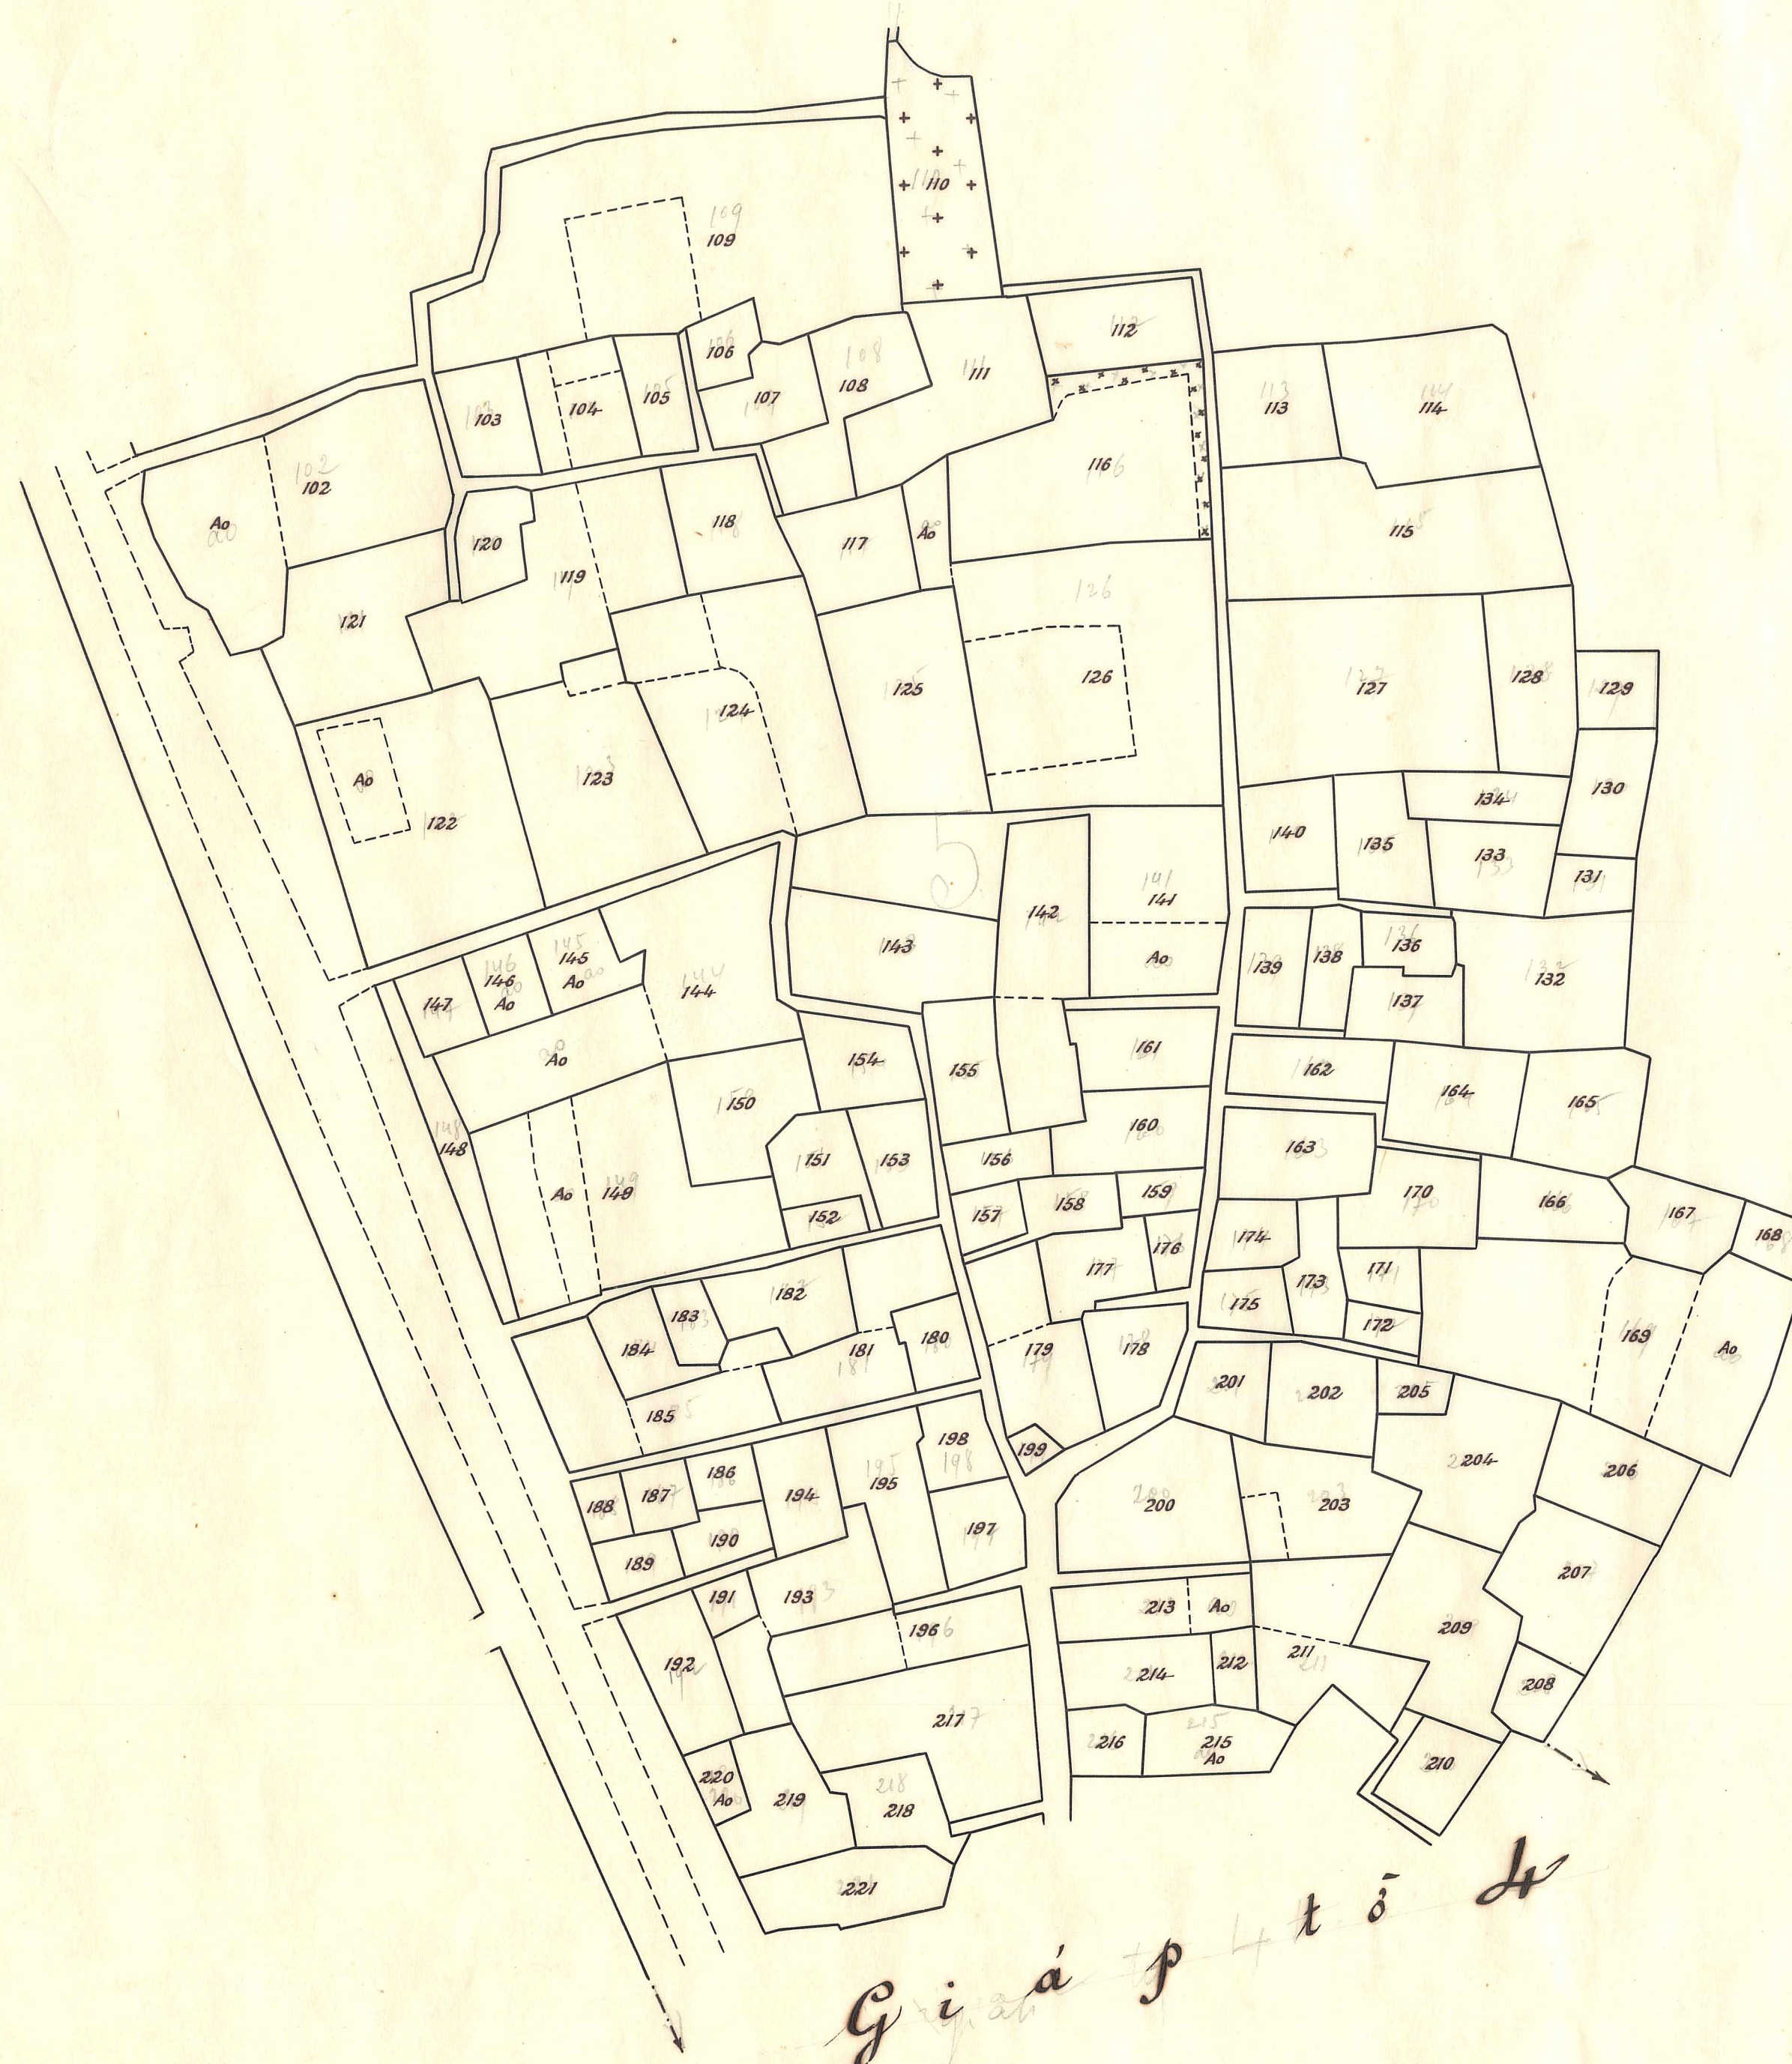

Giáp + t ð k

Tỉnh Hà Tây
 Huyện Ứng Hòa
 Xã Viên Nội
 Thôn Trung Thuồng
 Lập thành 7 tổ, tổ số 3
 Từ thửa số 1 đến thửa số 221

Thôn Trung-Thông

Lập thành 7 tờ, tờ số 3

Từ thừa số 1 đến thừa số 22

Bản đồ giải thửa
Tỷ lệ: 1/1.000

Tỷ lệ: 1/1.000

Vẽ ngày 1 tháng 3 năm 1968

Hội họa: Nguyễn Văn Thịnh